


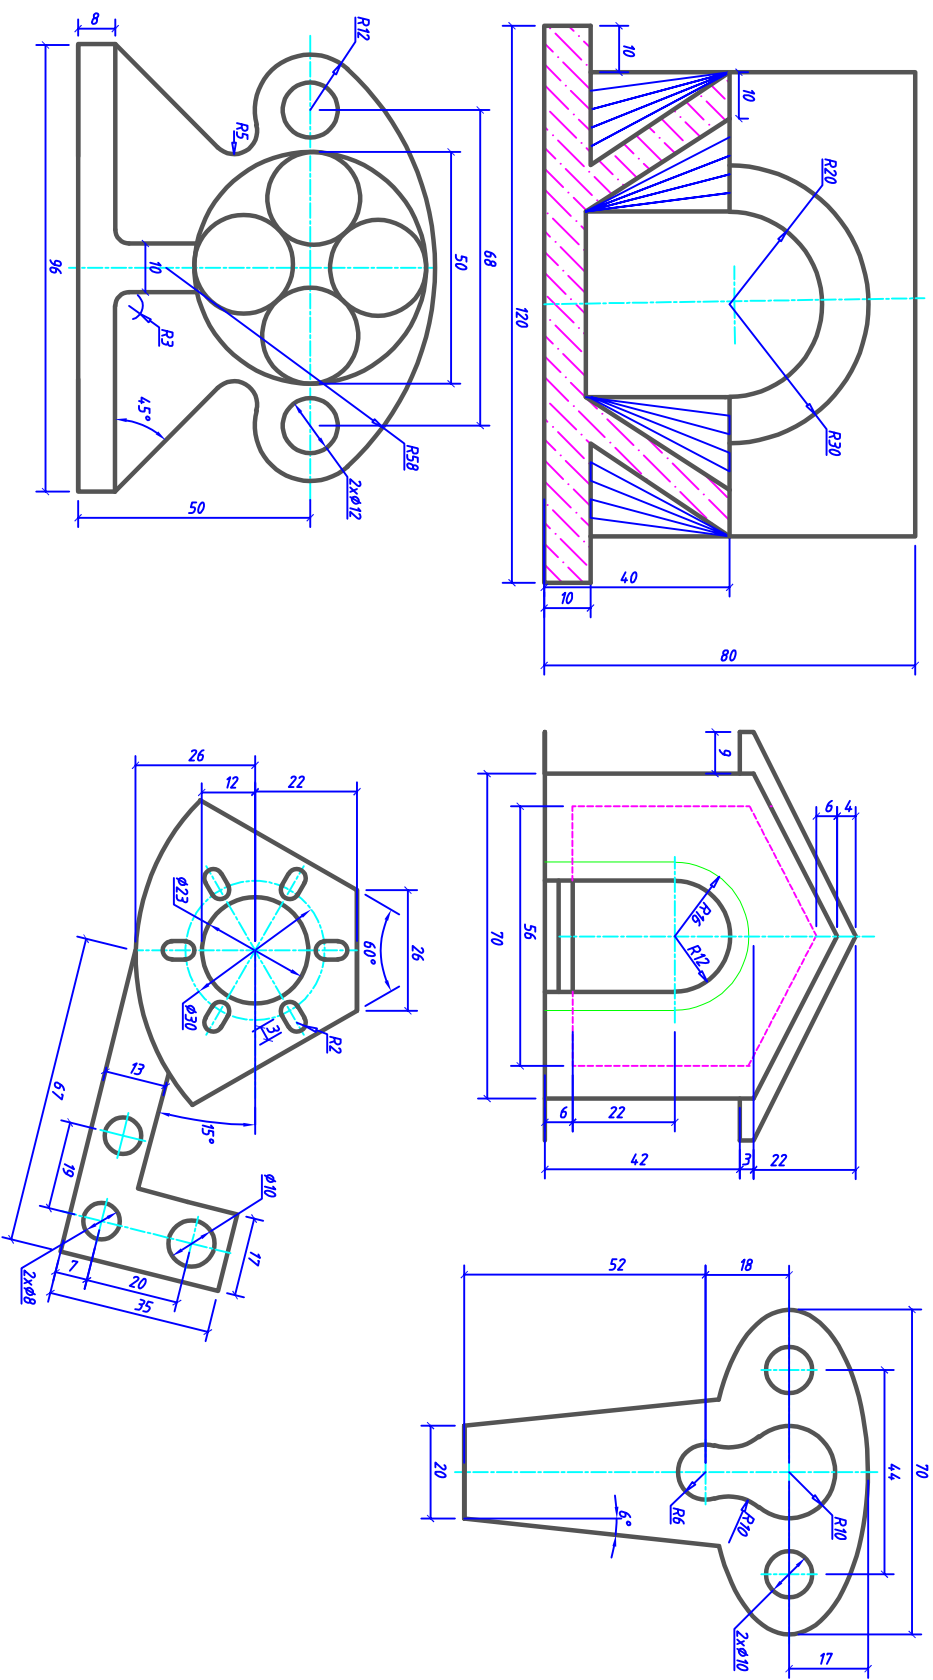

平面图形的尺寸标注

比例 1:1 成绩

图号 NO-2

姓名 DY 22.08

班级